


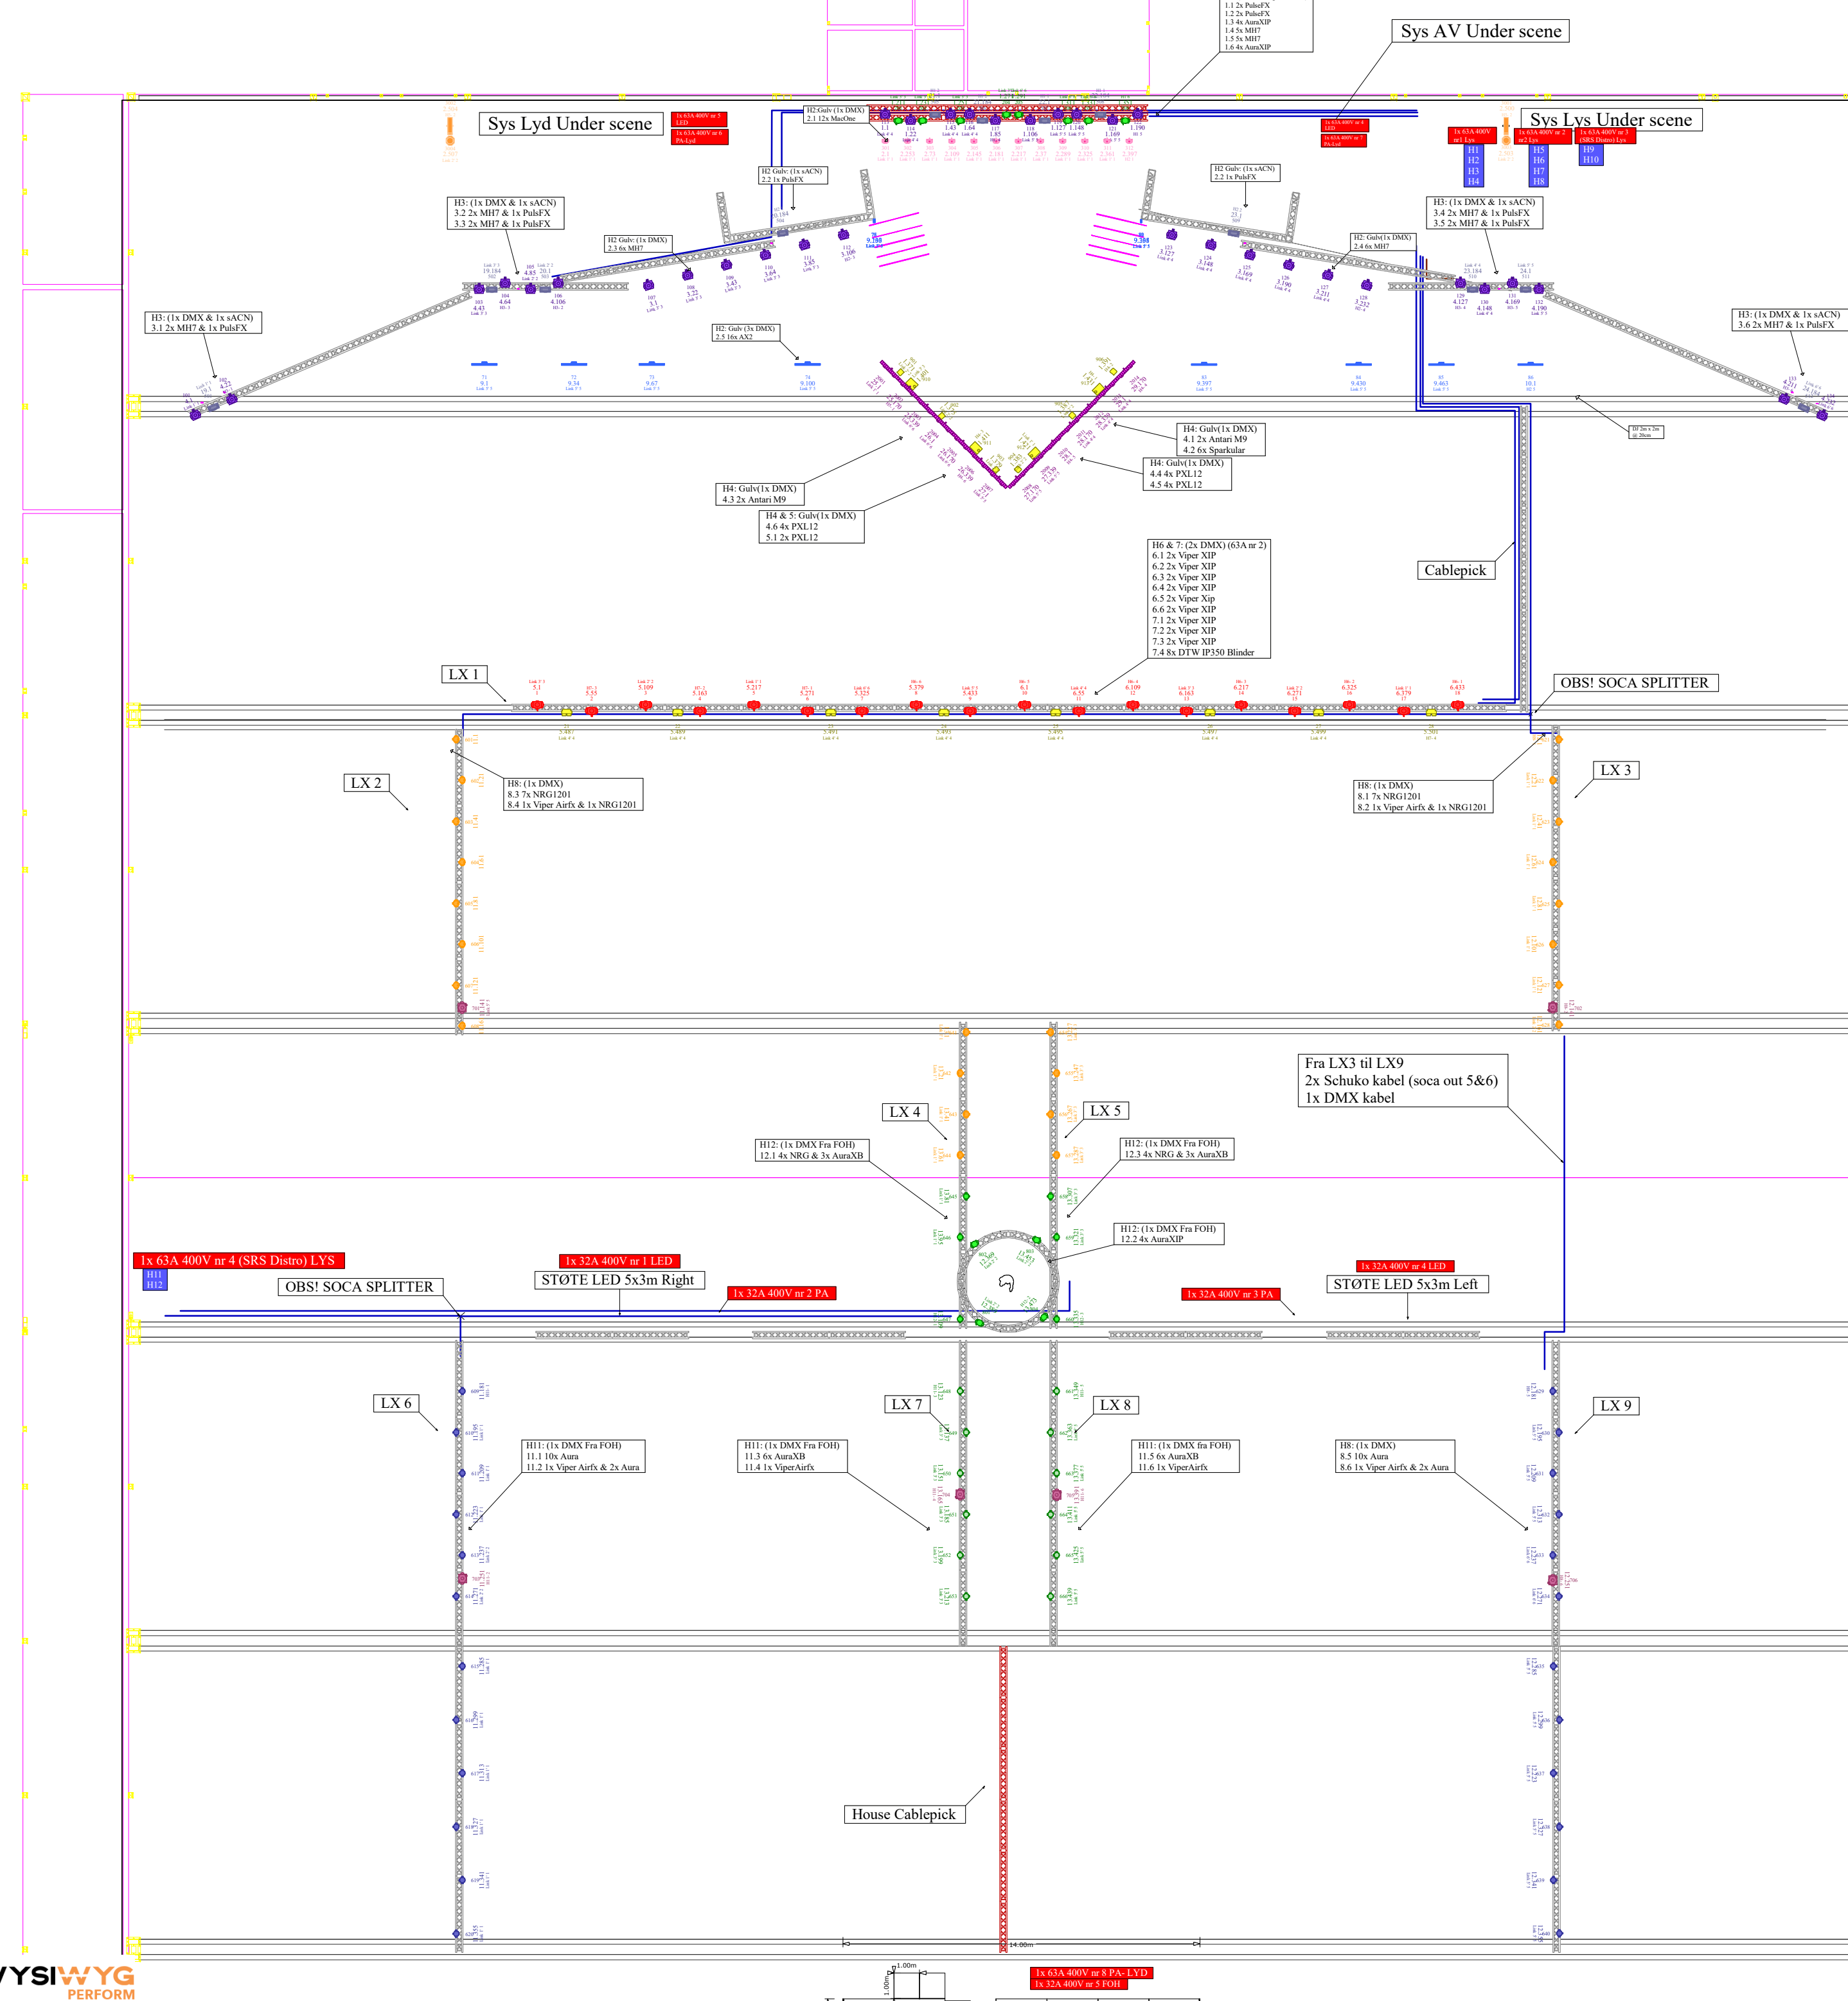

ZZAE25	
Lighting Design:	OT
Assistant:	
Director:	
Scenic Design:	
Venue:	THE QUBE
Zero Date:	9-12 Okt
Printed:	Oct/01/25
Printed By:	OltiTsako
File:	ZZAE25_v1.wyg

NOTES

- Hazers, smoke, and sparks machines must be turned off.

- All fixtures to have safety wires

- All truss to have Pins and R-clips

- Rigging safety gear to be supplied by EHS (HMS, helmet)

- LED Wall Delivered by KLS AS

Contacts:

Event Coordinator: Magnus (Tel: 41108888)

Production Manager: Morten (tel: 93211736)

Stage Lights: Olti (tel: 48623343)

Topp rigg: Peder (tel: 92439456)

Legend

Symbol	Name	Count	Mode	# Channels	Wattage
	Rush MH7	34		21	372
	MAC Viper XIP	18	Basic	54	759
	MAC One	12	Basic	36	168
	Pulse Panel FX	12	183CH Full Ctrl	183	1750
	Nick NRG 1201	24	20 Channel	20	340
	MAC Viper AirFX	6	16-Bit	20	1225
	Mac Aura XIP	12	Compact	20	340
	MAC Aura	30	Std.	14	260
	DTW Blinder 350 IP v1.2	8	2	2	310
	MAC Aura XB	12	Std.	14	400
	AX2-100	16	DIM-RGB	33	160
	VDO Fatron 20 1000 Diffusion	68	P3 10 Hybrid	33	200
	Colorado PXL Curve 12 Full PXL	14	Full PXL	169	800
	Sparkular	6		2	5
	Antari M9	4	Extended	3	1500
	MDG ATMe Hazer	2		3	715
	AF-1	2		1	120