



MainStage

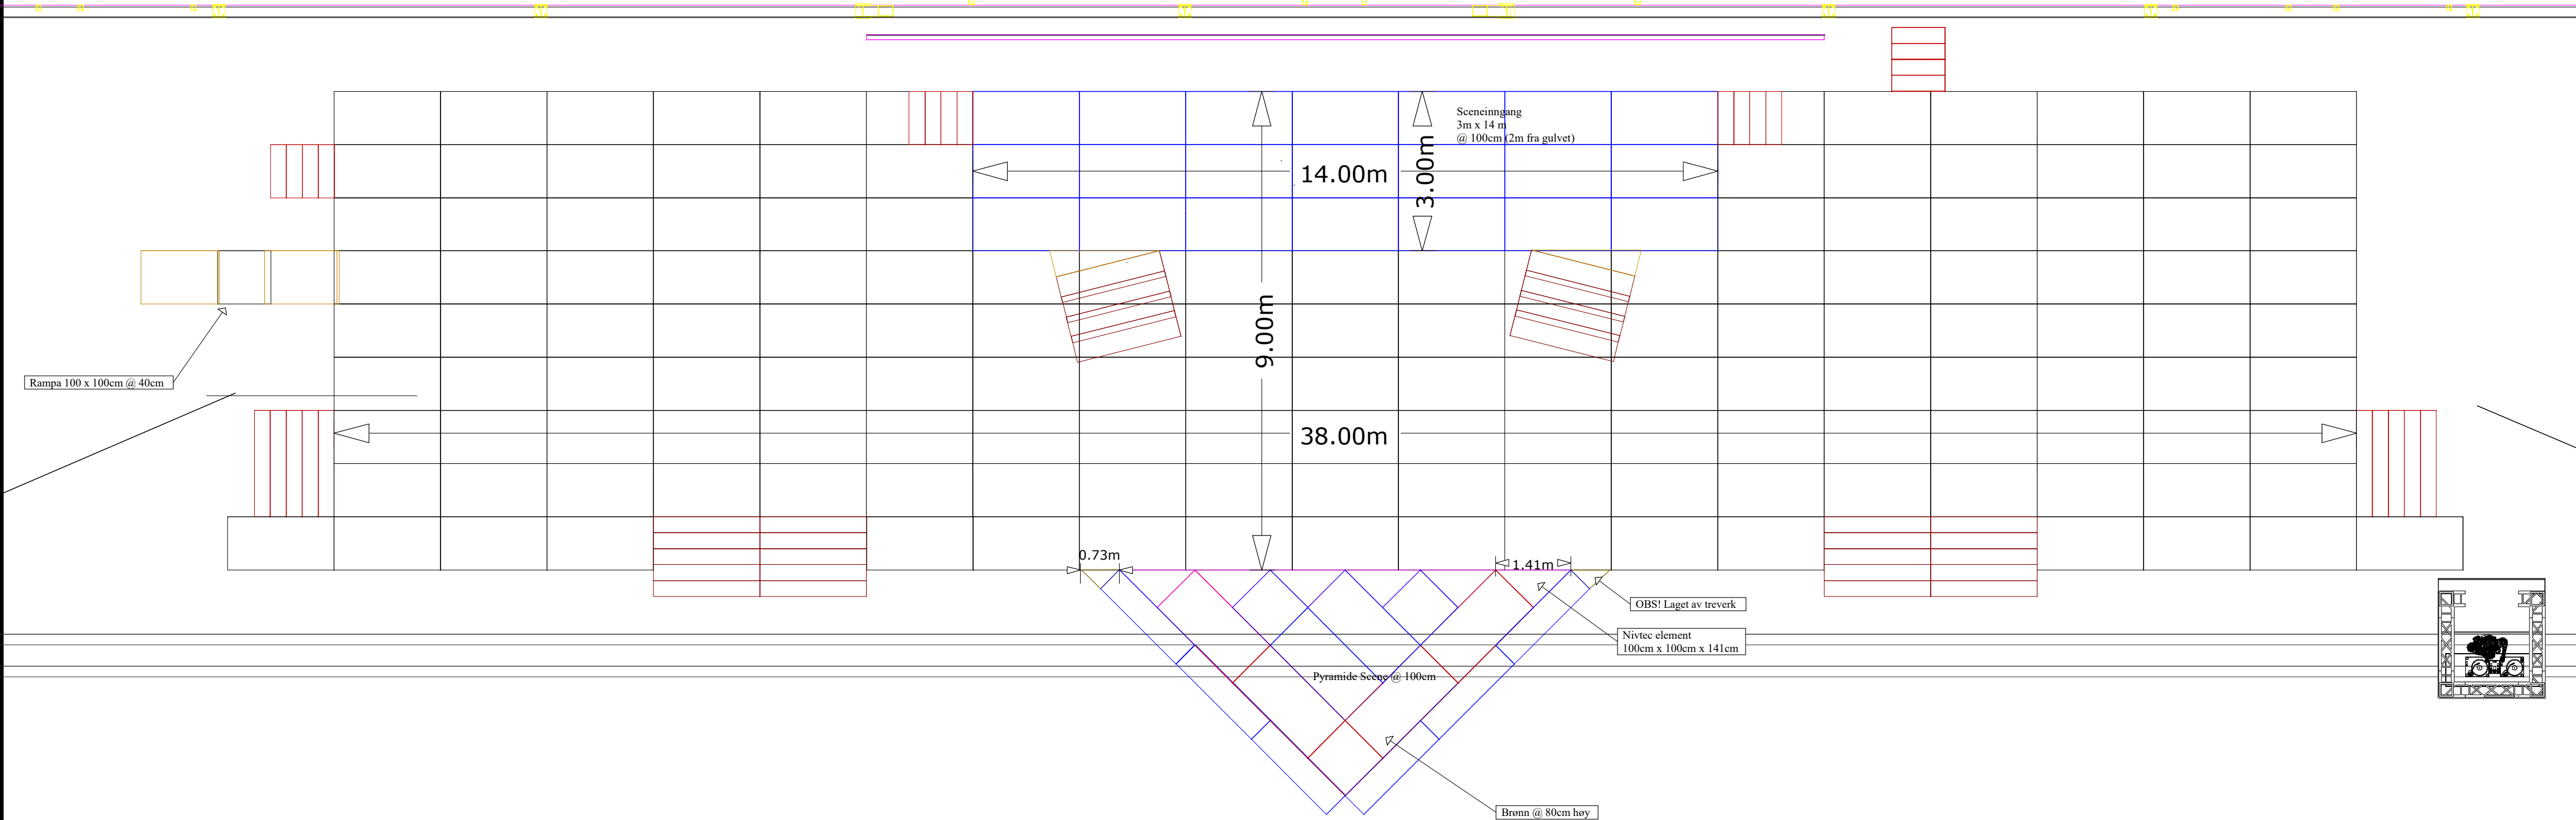

FOH

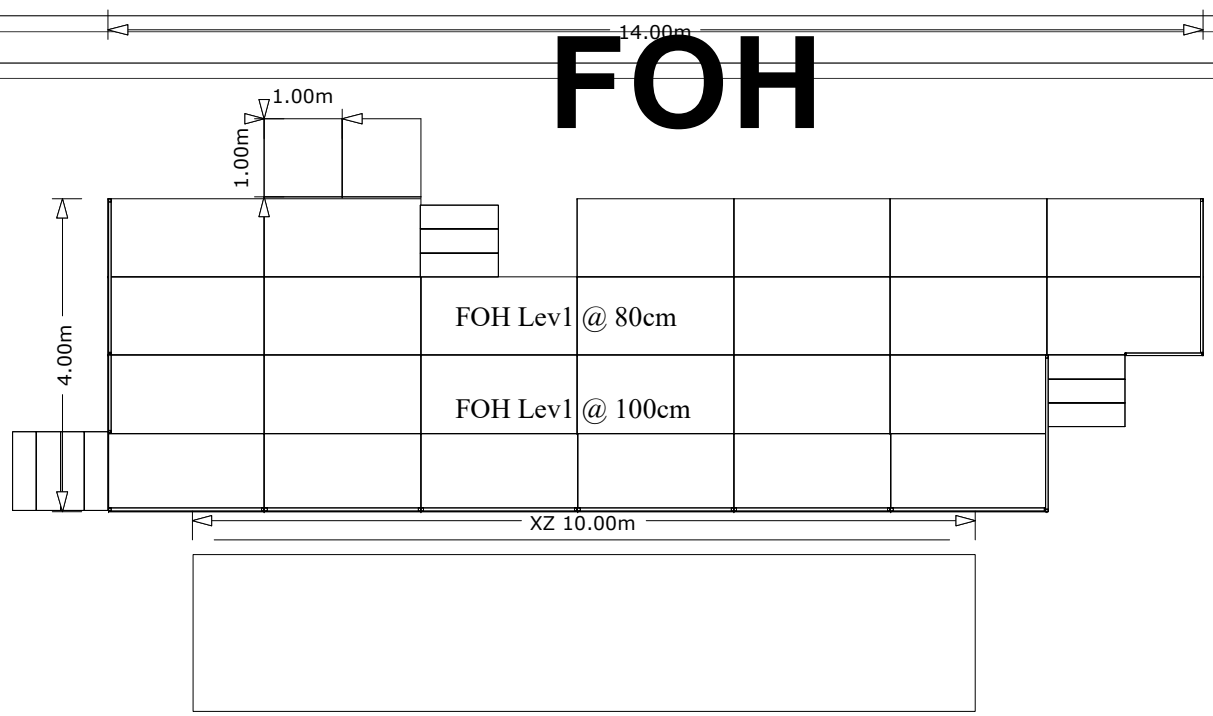

Tolk

Tolk 14m x 2m @ 40cm

