


| ZZAE25           |               |
|------------------|---------------|
| Lighting Design: | OT            |
| Assistant:       |               |
| Director:        |               |
| Scenic Design:   |               |
| Venue:           | THE QUBE      |
| Zero Date:       | 9-12 Okt      |
| Printed:         | Oct/01/25     |
| Printed By:      | OltiTsako     |
| File:            | ZZAE25_v1.wyg |

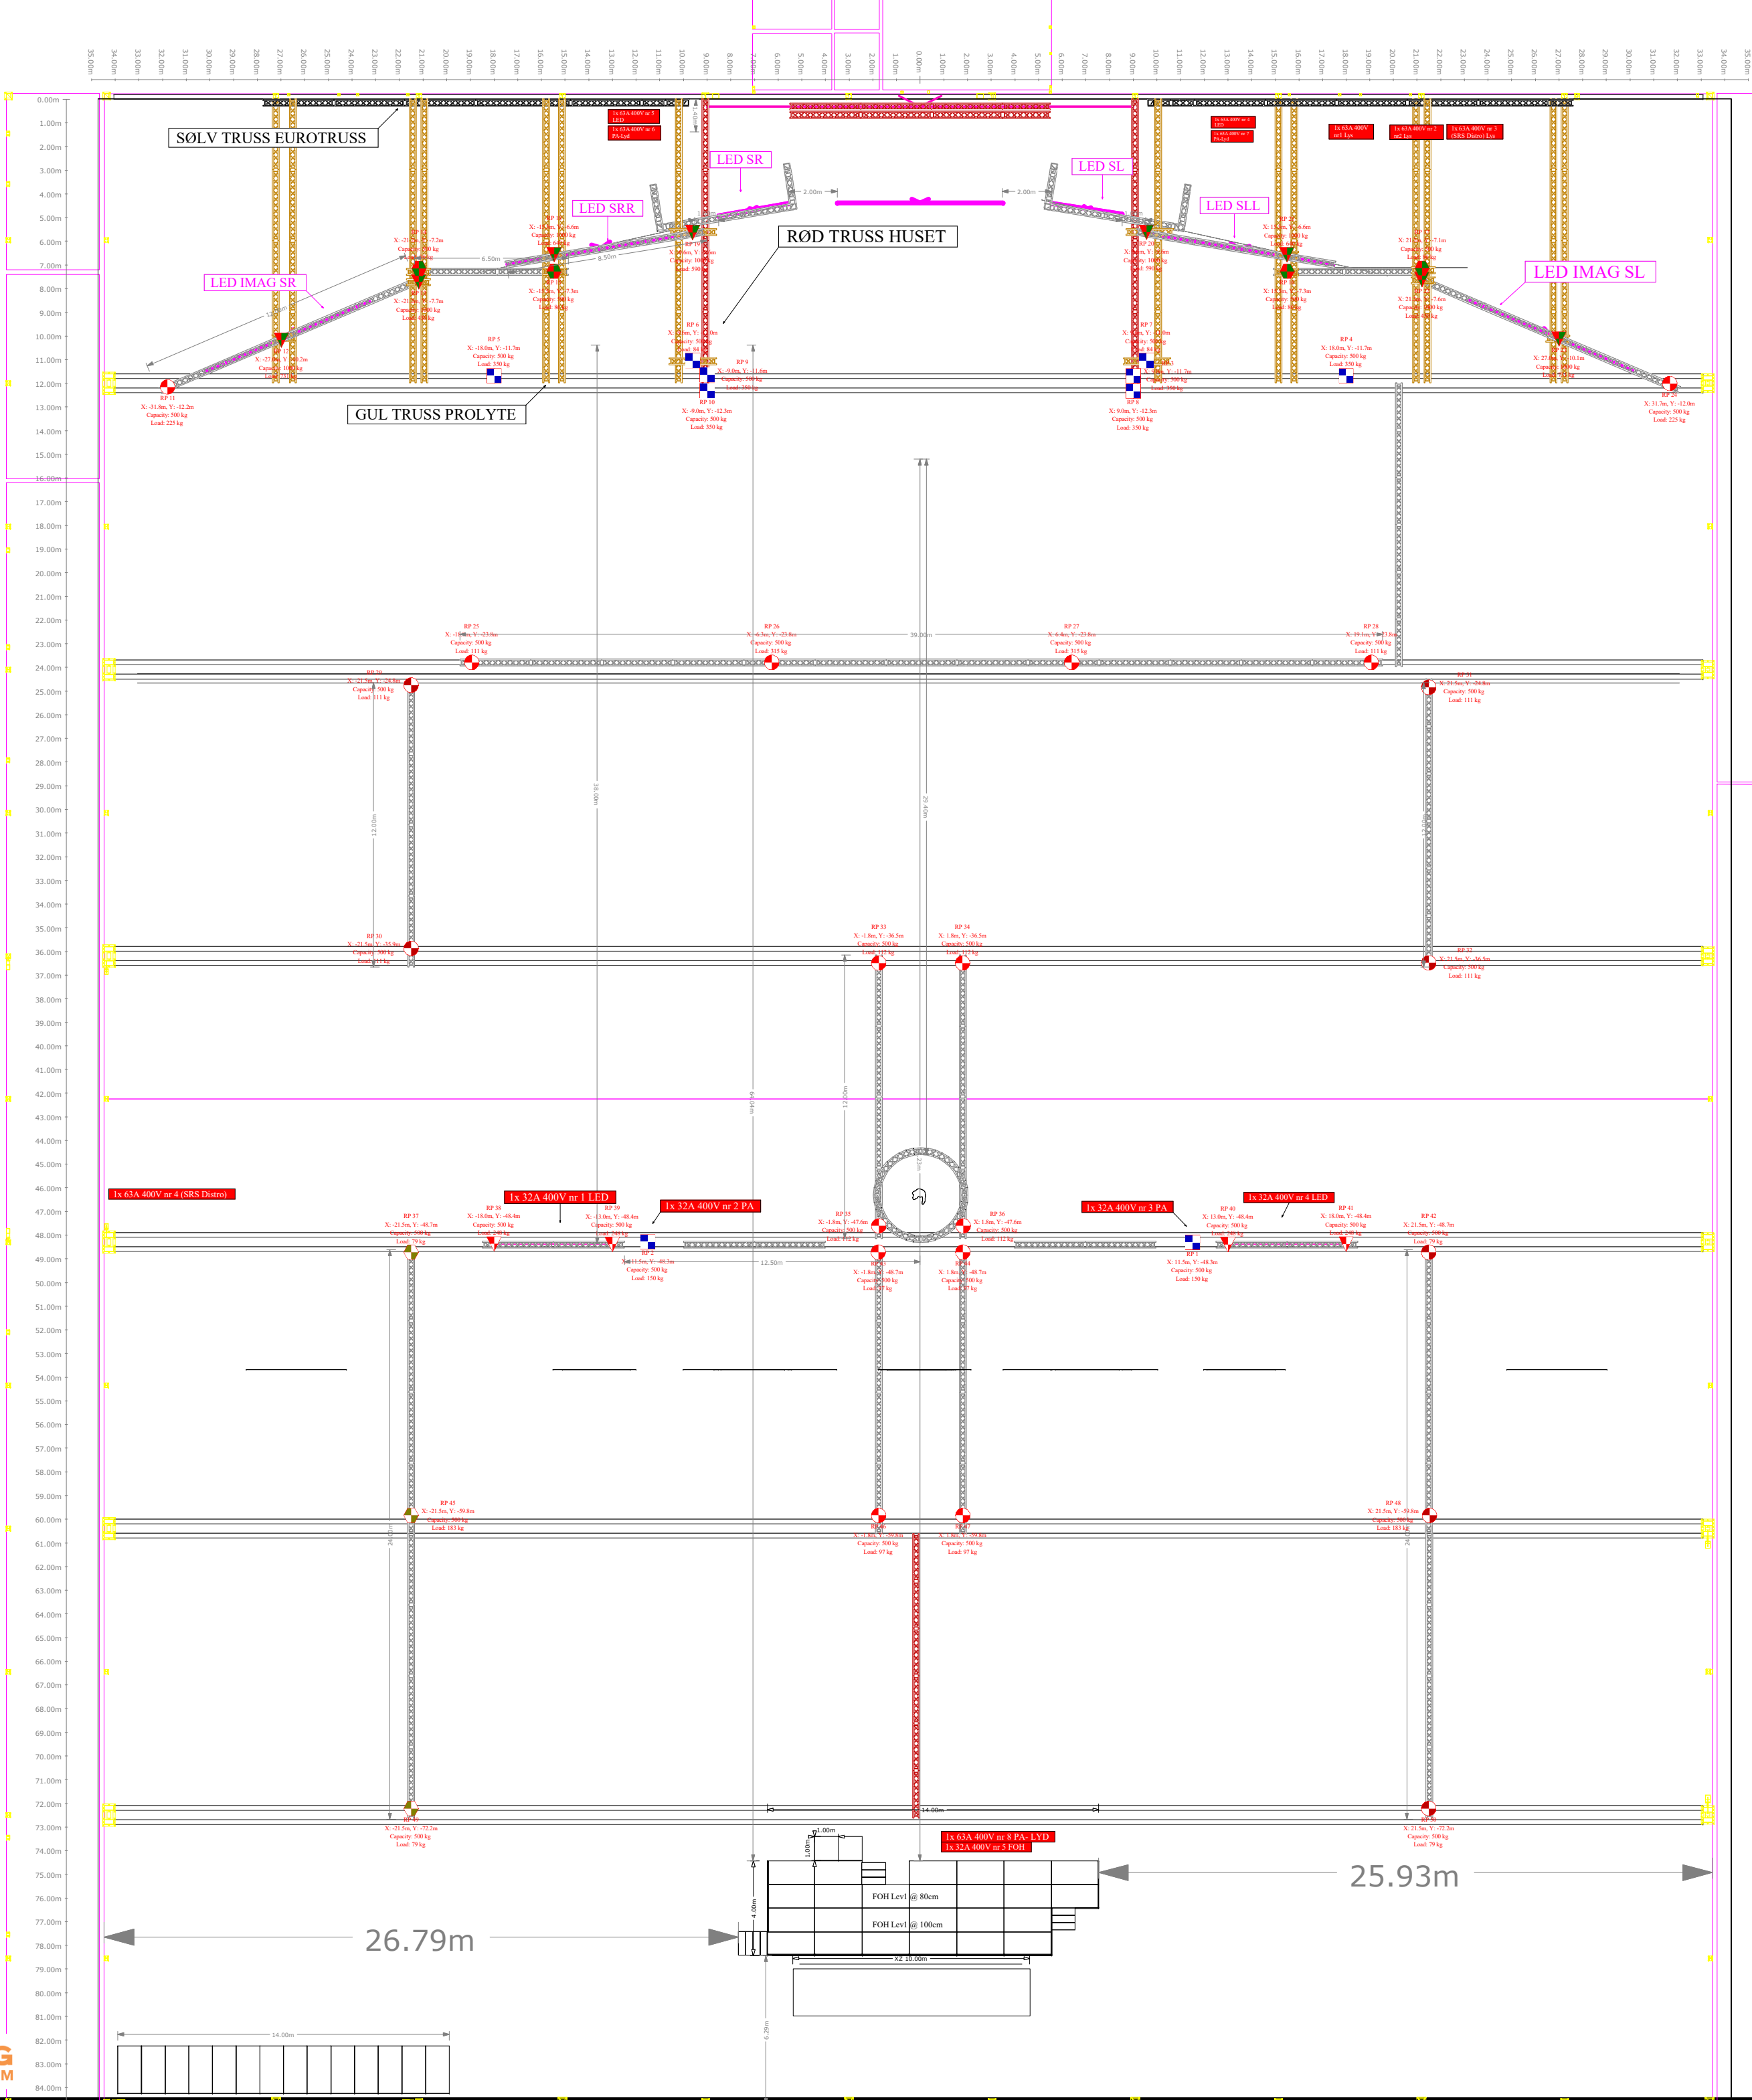

### Rigging Points List

| Venue: THE QUBE |         | Designer: OT |       | Oct/01/25  |           |          |                  |              |
|-----------------|---------|--------------|-------|------------|-----------|----------|------------------|--------------|
| Show: ZZAE25    |         | Assistant:   |       |            |           |          |                  |              |
| Name            | X       | Y            | Z     | Capacity   | Load      | Type     | Motor/Hoist Type | Chain Length |
| RP 1            | 11.50m  | -48.31m      | 0.10m | 500.00 kg  | 150.00 kg | Audio    | Exe D8+          | 24m          |
| RP 2            | -11.50m | -48.28m      | 0.10m | 500.00 kg  | 150.00 kg | Audio    | Exe D8+          | 24m          |
| RP 3            | 9.00m   | -11.68m      | 0.10m | 500.00 kg  | 350.00 kg | Audio    | Exe D8+          | 24m          |
| RP 4            | 18.00m  | -11.68m      | 0.10m | 500.00 kg  | 350.00 kg | Audio    | Exe D8+          | 24m          |
| RP 5            | -18.00m | -11.68m      | 0.10m | 500.00 kg  | 350.00 kg | Audio    | Exe D8+          | 24m          |
| RP 6            | -9.61m  | -11.04m      | 0.10m | 500.00 kg  | 84.00 kg  | Audio    | MT               | 24m          |
| RP 7            | 9.55m   | -11.04m      | 0.10m | 500.00 kg  | 84.00 kg  | Audio    | MT               | 24m          |
| RP 8            | 9.00m   | -12.34m      | 0.10m | 500.00 kg  | 350.00 kg | Audio    | Exe D8+          | 24m          |
| RP 9            | -9.00m  | -11.64m      | 0.10m | 500.00 kg  | 350.00 kg | Audio    | Exe D8+          | 24m          |
| RP 10           | -9.00m  | -12.32m      | 0.10m | 500.00 kg  | 350.00 kg | Audio    | Exe D8+          | 24m          |
| RP 11           | -31.79m | -12.16m      | 6.60m | 500.00 kg  | 224.20 kg | Lighting | Exe D8+          | 24m          |
| RP 12           | -26.98m | -10.18m      | 6.60m | 1000.00 kg | 731.00 kg | Video    | Exe D8+          | 24m          |
| RP 13           | -21.18m | -7.72m       | 6.60m | 1000.00 kg | 430.00 kg | Video    | Exe D8+          | 24m          |
| RP 14           | -21.17m | -7.15m       | 6.60m | 500.00 kg  | 85.75 kg  | Scenic   | MT               | 12m          |
| RP 15           | -15.47m | -7.27m       | 6.60m | 500.00 kg  | 85.75 kg  | Scenic   | MT               | 12m          |
| RP 16           | 15.50m  | -7.27m       | 6.60m | 500.00 kg  | 85.75 kg  | Scenic   | MT               | 12m          |
| RP 17           | 21.22m  | -7.14m       | 6.60m | 500.00 kg  | 85.75 kg  | Scenic   | MT               | 12m          |
| RP 18           | -15.46m | -6.56m       | 6.60m | 1000.00 kg | 640.00 kg | Video    | Exe D8+          | 24m          |
| RP 19           | -9.61m  | -5.63m       | 6.60m | 1000.00 kg | 590.00 kg | Video    | Exe D8+          | 24m          |
| RP 20           | 9.56m   | -5.62m       | 6.60m | 1000.00 kg | 590.00 kg | Video    | Exe D8+          | 24m          |
| RP 21           | 15.49m  | -6.57m       | 6.60m | 1000.00 kg | 640.00 kg | Video    | Exe D8+          | 24m          |
| RP 22           | 21.21m  | -7.62m       | 6.60m | 1000.00 kg | 430.00 kg | Video    | Exe D8+          | 24m          |
| RP 23           | 27.00m  | -10.12m      | 6.60m | 1000.00 kg | 731.00 kg | Video    | Exe D8+          | 24m          |
| RP 24           | 31.68m  | -12.01m      | 6.60m | 500.00 kg  | 224.20 kg | Lighting | Exe D8+          | 24m          |
| RP 25           | -18.94m | -23.79m      | 7.60m | 500.00 kg  | 110.50 kg | Lighting | Exe D8+          | 24m          |
| RP 26           | -6.27m  | -23.79m      | 7.60m | 500.00 kg  | 314.50 kg | Lighting | Exe D8+          | 24m          |
| RP 27           | 6.40m   | -23.79m      | 7.60m | 500.00 kg  | 314.50 kg | Lighting | Exe D8+          | 24m          |
| RP 28           | 19.07m  | -23.79m      | 7.60m | 500.00 kg  | 110.50 kg | Lighting | Exe D8+          | 24m          |
| RP 29           | -21.50m | -24.75m      | 7.60m | 500.00 kg  | 110.60 kg | Lighting | Exe D8+          | 12m          |
| RP 30           | -21.50m | -35.87m      | 7.60m | 500.00 kg  | 110.60 kg | Lighting | Exe D8+          | 12m          |
| RP 31           | 21.50m  | -24.84m      | 7.60m | 500.00 kg  | 110.60 kg | Lighting | Exe D8+          | 12m          |
| RP 32           | 21.50m  | -36.48m      | 7.60m | 500.00 kg  | 110.60 kg | Lighting | Exe D8+          | 12m          |
| RP 33           | -1.75m  | -36.49m      | 7.60m | 500.00 kg  | 112.00 kg | Lighting | Exe D8+          | 24m          |
| RP 34           | 1.79m   | -36.49m      | 7.60m | 500.00 kg  | 112.00 kg | Lighting | Exe D8+          | 24m          |
| RP 35           | -1.75m  | -47.61m      | 7.60m | 500.00 kg  | 112.00 kg | Lighting | Exe D8+          | 24m          |
| RP 36           | 1.82m   | -47.61m      | 7.60m | 500.00 kg  | 112.00 kg | Lighting | Exe D8+          | 24m          |
| RP 37           | -21.50m | -48.72m      | 7.60m | 500.00 kg  | 78.56 kg  | Scenic   | MT               | 12m          |
| RP 38           | -18.00m | -48.37m      | 0.10m | 500.00 kg  | 247.50 kg | Video    | Exe D8+          | 24m          |
| RP 39           | -13.00m | -48.39m      | 0.10m | 500.00 kg  | 247.50 kg | Video    | Exe D8+          | 24m          |
| RP 40           | 13.00m  | -48.40m      | 0.10m | 500.00 kg  | 247.50 kg | Video    | Exe D8+          | 24m          |
| RP 41           | 18.00m  | -48.38m      | 0.10m | 500.00 kg  | 247.50 kg | Video    | Exe D8+          | 24m          |
| RP 42           | 21.50m  | -48.72m      | 7.60m | 500.00 kg  | 78.56 kg  | Lighting | Exe D8+          | 12m          |
| RP 43           | -1.77m  | -48.72m      | 7.60m | 500.00 kg  | 96.50 kg  | Lighting | Exe D8+          | 24m          |
| RP 44           | 1.80m   | -48.72m      | 7.60m | 500.00 kg  | 96.50 kg  | Lighting | Exe D8+          | 24m          |
| RP 45           | -21.50m | -59.84m      | 7.60m | 500.00 kg  | 182.28 kg | Scenic   | MT               | 12m          |
| RP 46           | -1.76m  | -59.84m      | 7.60m | 500.00 kg  | 96.50 kg  | Lighting | Exe D8+          | 24m          |
| RP 47           | 1.80m   | -59.84m      | 7.60m | 500.00 kg  | 96.50 kg  | Lighting | Exe D8+          | 24m          |
| RP 48           | 21.53m  | -59.84m      | 7.60m | 500.00 kg  | 182.28 kg | Lighting | Exe D8+          | 12m          |
| RP 49           | -21.50m | -72.22m      | 7.60m | 500.00 kg  | 78.56 kg  | Scenic   | MT               | 12m          |
| RP 50           | 21.50m  | -72.22m      | 0.10m | 500.00 kg  | 78.56 kg  | Lighting | Exe D8+          | 12m          |